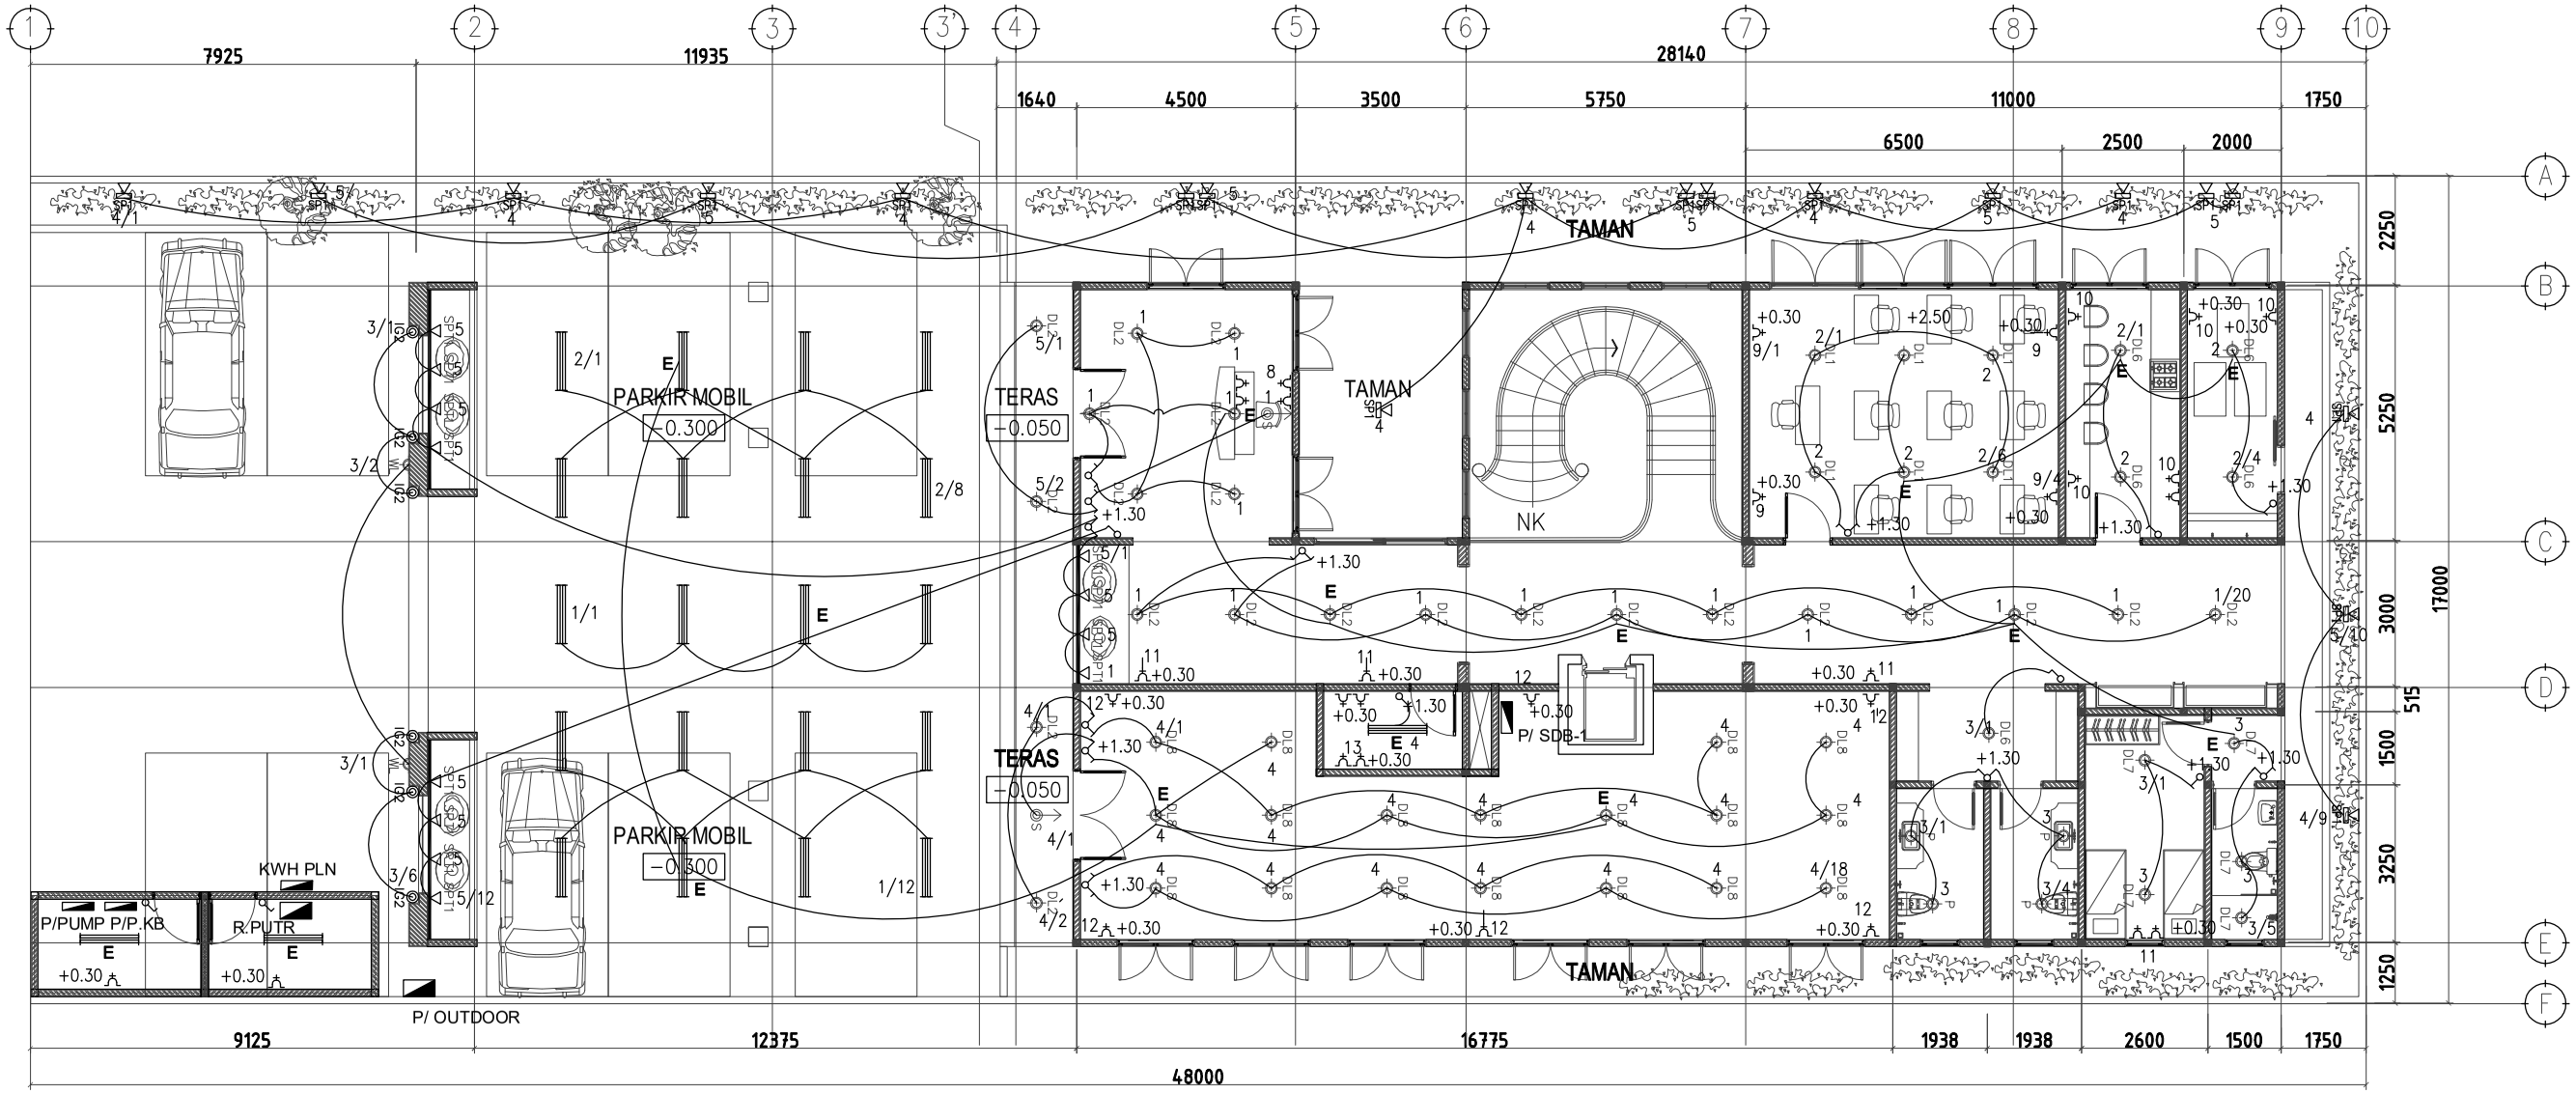


## DENAH INSTALASI PENERANGAN LT.1

SKALA : 1 / 150

FOR CONSTRUCTION

yudha narta
architecture . interior . decoration
email : yudha_gumulja@cbn.net.id

| PROJECT : | DRAWING TITLE : | DRAWING INFORMATION | PARAF | NO. | DATE REVISION | NO. | DATE REVISION | DATE | CODE | SHEET NUMBER |
|---|---|---|---|---|---|---|---|---|---|---|
| .\Bridal Logo.jpg DEPOK - JAWA BARAT | DENAH INSTALASI PENERANGAN LANTAI 1 | DRAWN BY : – | | 01. | – | 04. | – | 11/05/23 | EL | EL-02 |
| | | CHECKED BY : – | | 02. | – | 05. | – | | | |
| | | P.I.C. : – | | 03. | – | 06. | – | PROJECT NO. : – | | |