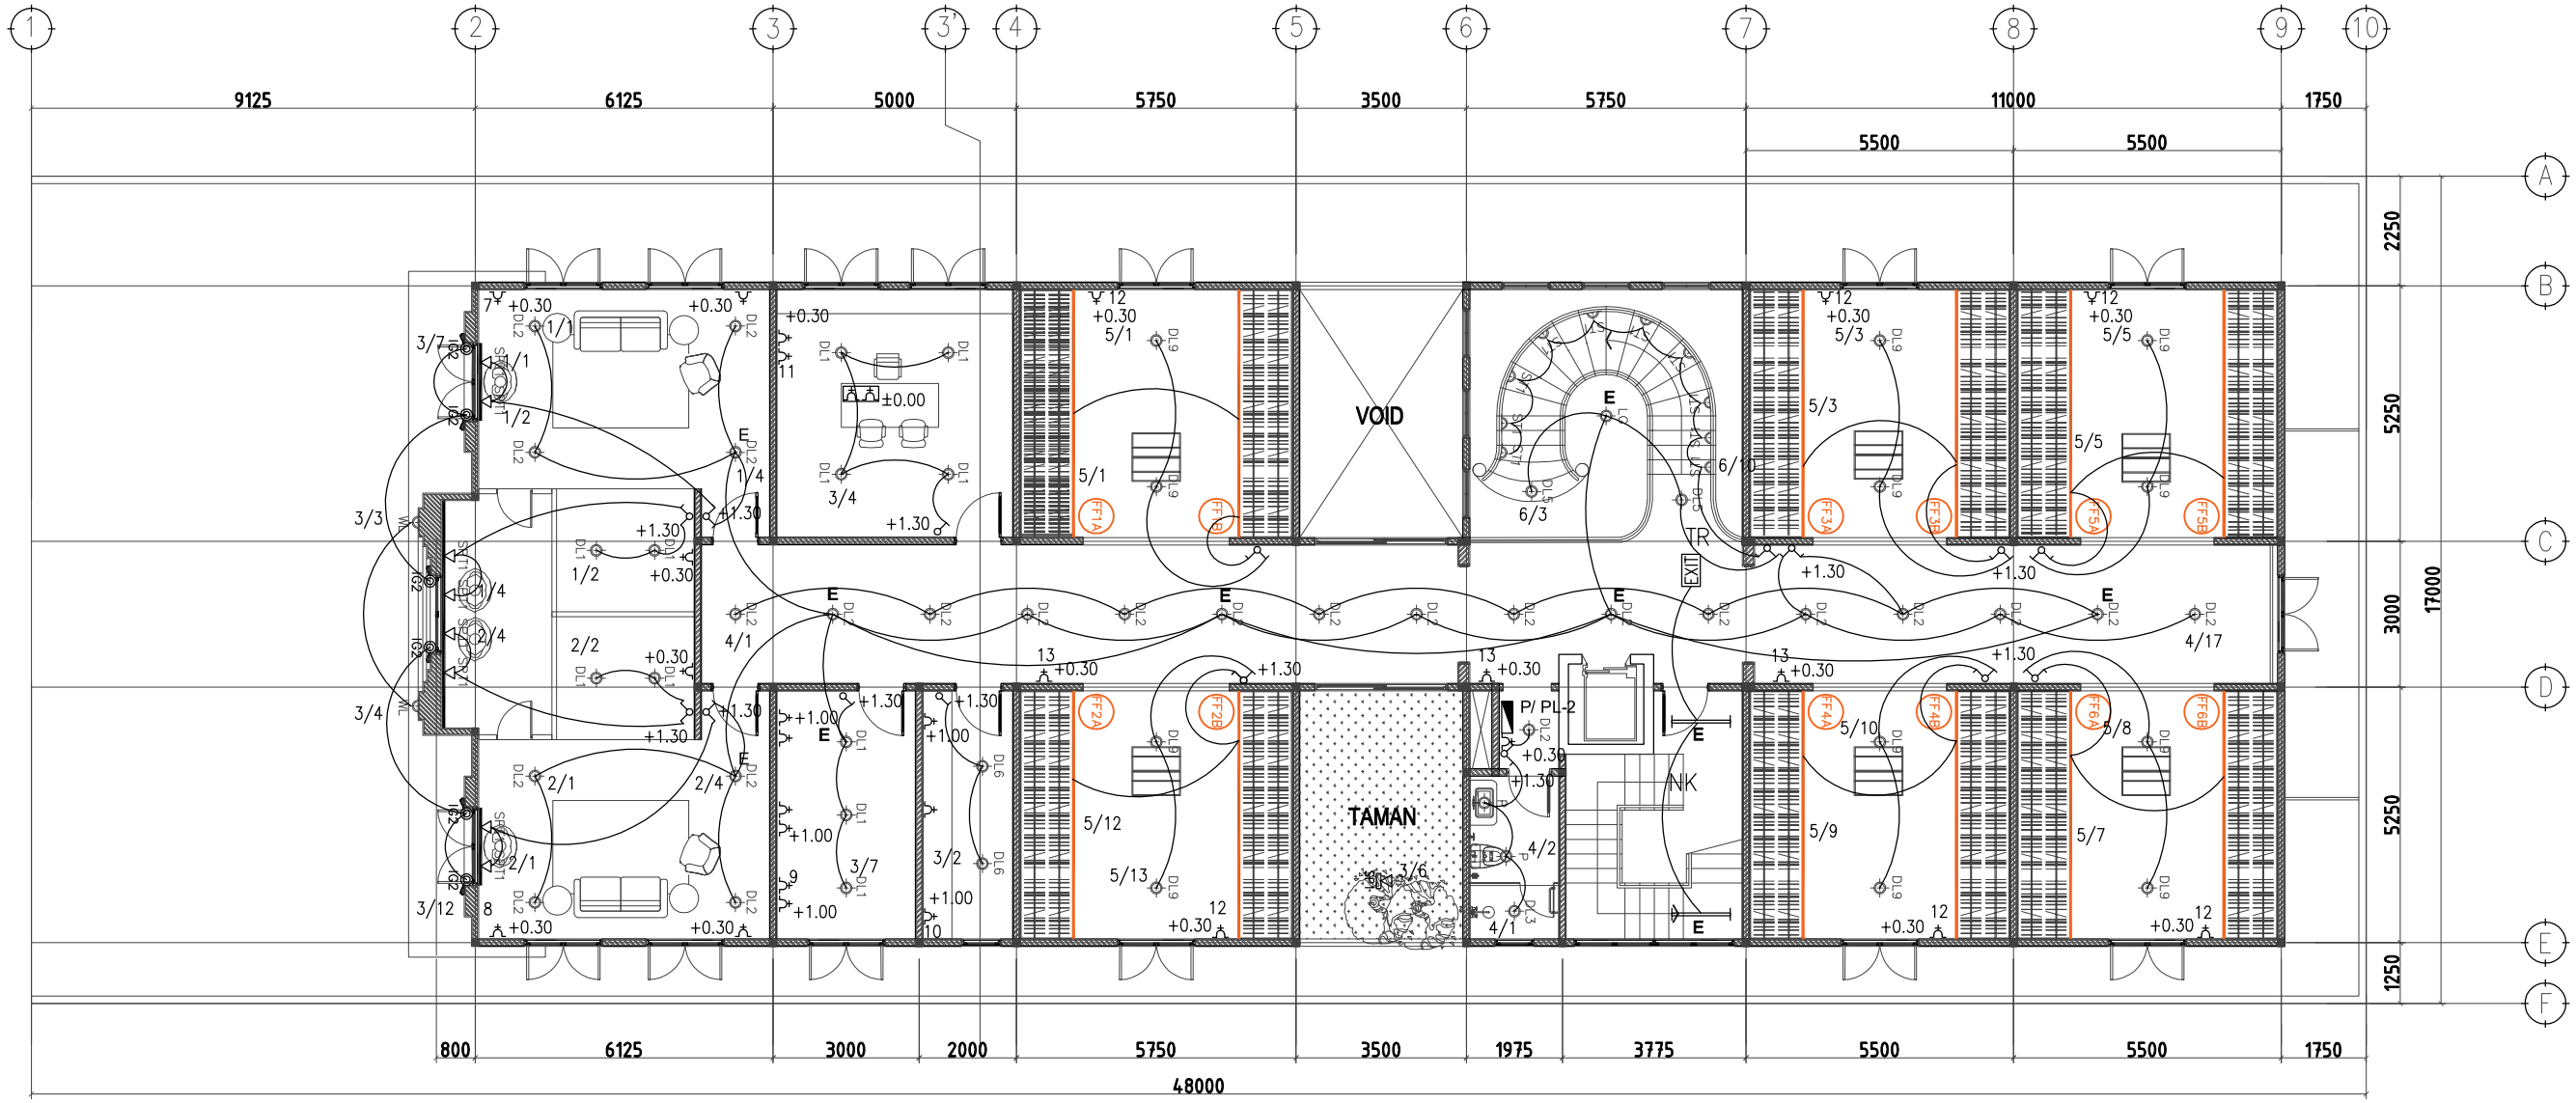

DENAH INSTALASI PENERANGAN LT.2

SKALA : 1 / 150

FOR CONSTRUCTION

yudha narta architecture . interior . decoration email : yudha_gumulja@cbn.net.id	PROJECT :	DRAWING TITLE :	DRAWING INFORMATION	PARAF	NO.	DATE REVISION	NO.	DATE REVISION	DATE	CODE	SHEET NUMBER
	.\Bridal Logo.jpg DEPOK - JAWA BARAT	DENAH INSTALASI PENERANGAN LANTAI 2	DRAWN BY : –		01.	–	04.	–	11/05/23	EL	EL-03
			CHECKED BY : –		02.	–	05.	–			
			P.I.C. : –		03.	–	06.	–	PROJECT NO. : –		