VALVE
CHECK VALVE
FLEXIBLE JOINT
STRAINEER

PIPA AIR BERSIH PPR PN 10 EX ATP TORO
PIPA AIR PANAS PPR PN 20 EX ATP TORO
TANGKI AIR FIBERGLASS
POMPA TRANSFER & BOOSTER EX GRUNDFOS
VALVE & ACCESSORIES EX KITZ
AB (S) : AIR BERSIH
AP (S) : AIR PANAS SUPLAY
AP (R) : AIR PANAS RETRUN
GV : GATE VALVE
CV : CHECK VALVE
FJ : FLEXIBLE JOINT
STR : STRAINEER
PT : POMPA TRANSFER

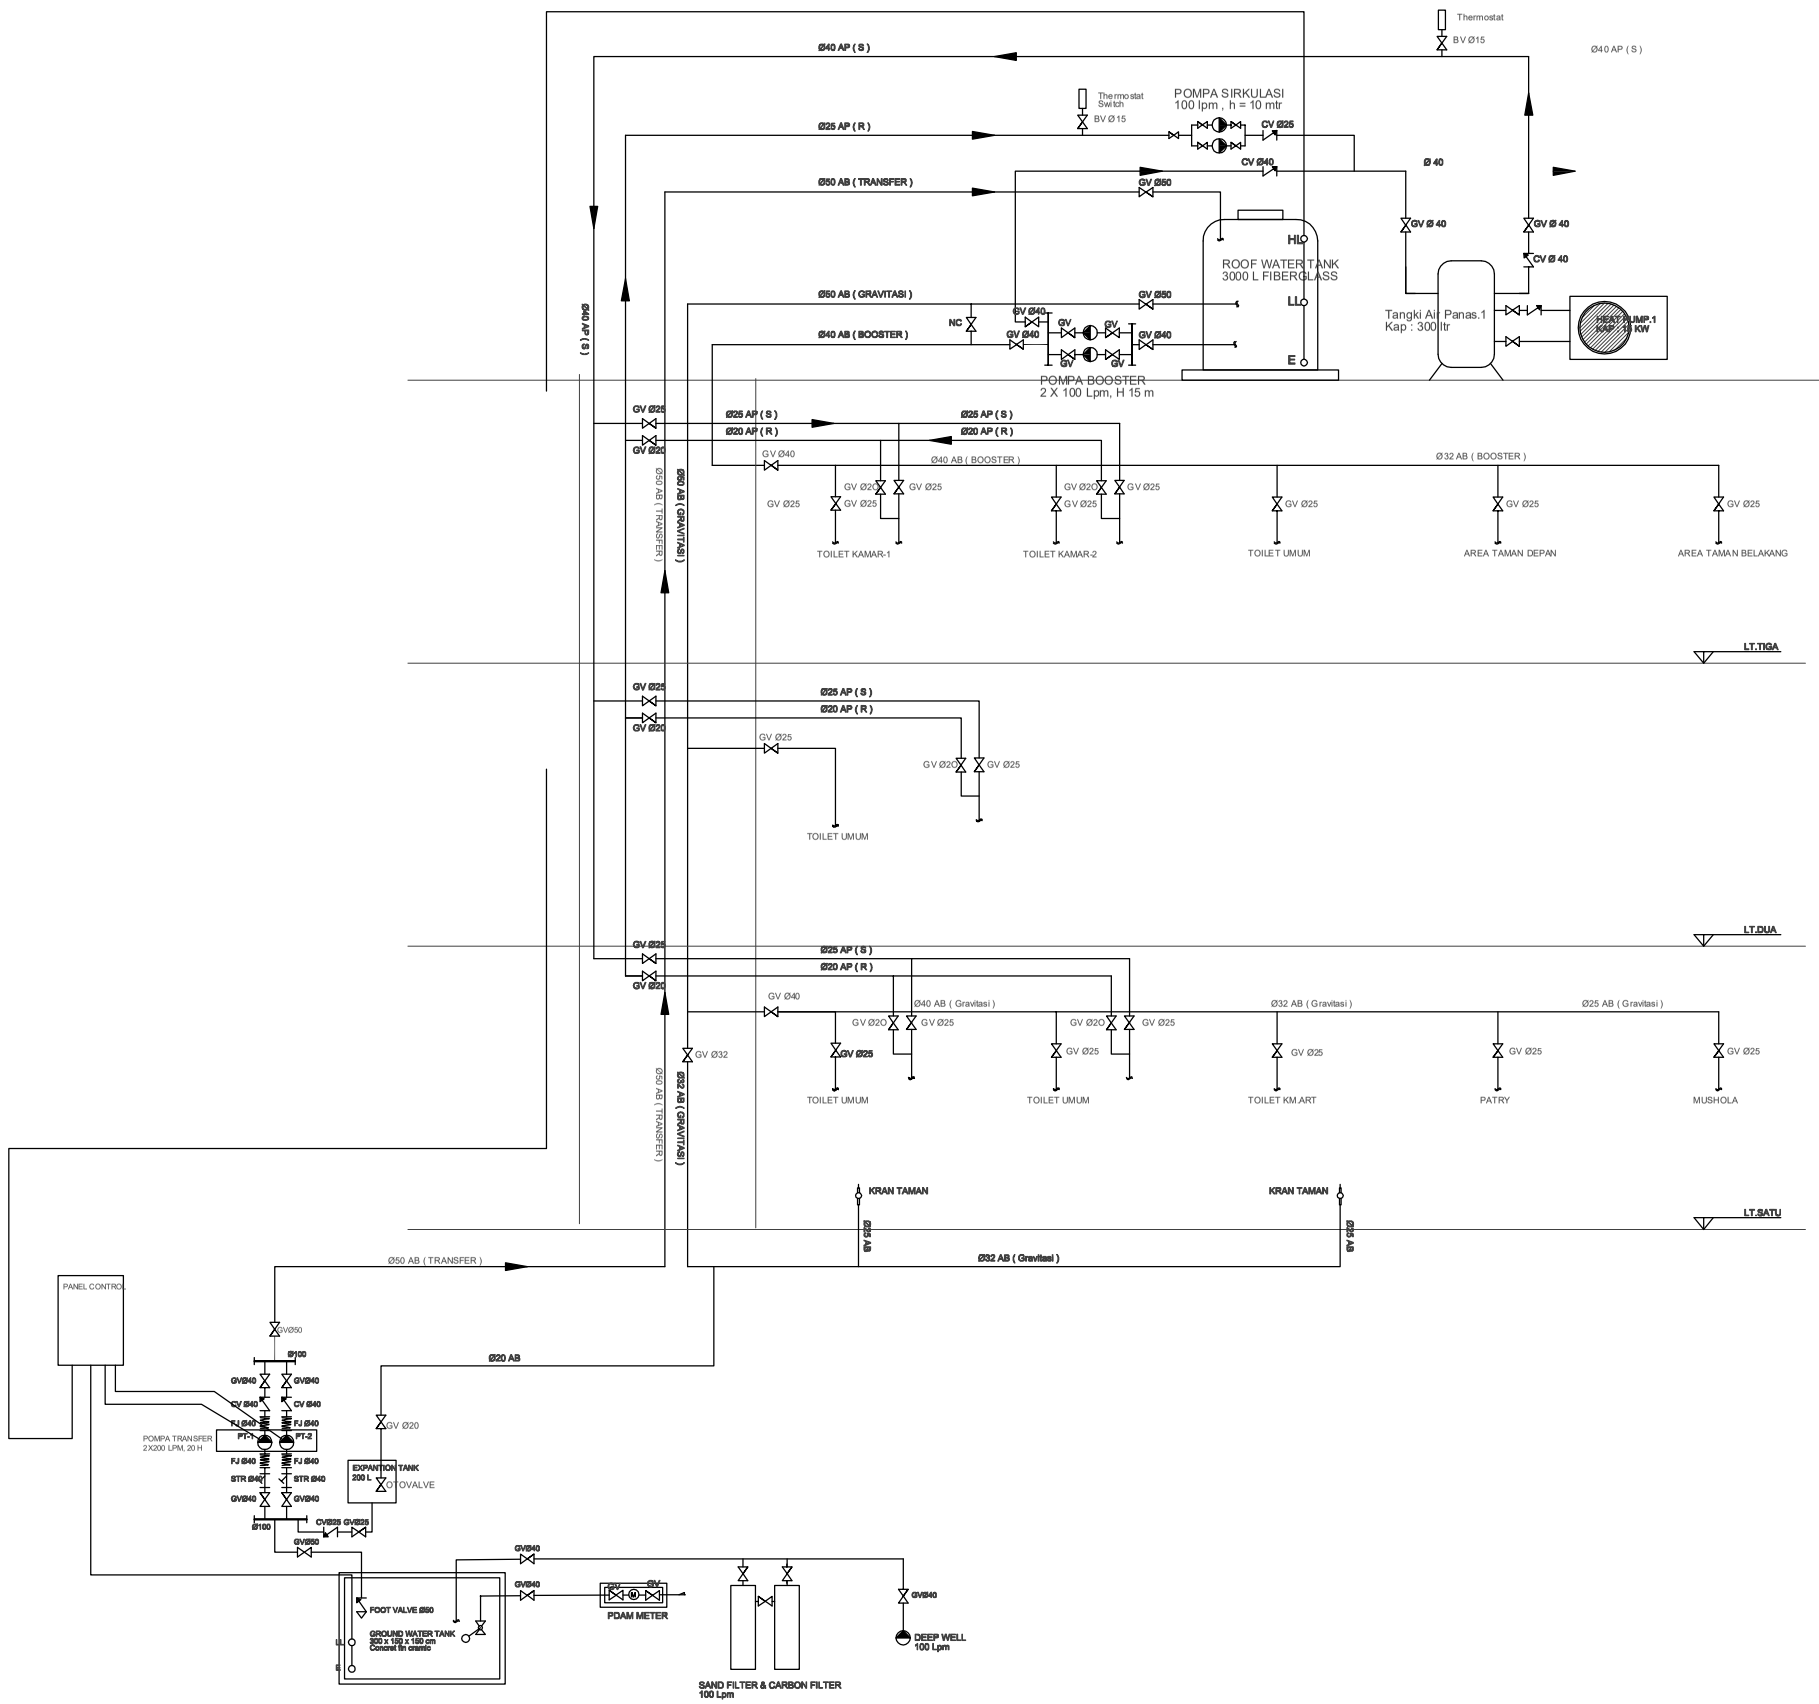

SKEMATIK PIPA AIR BERSIH DAN PANAS

SKALA : NTS

FOR CONSTRUCTION

yudha narta architecture . interior . decoration email : yudha_gumulja@cbn.net.id	PROJECT : DEPOK - JAWA BARAT	DRAWING TITLE : SKEMATIK PIP AIR BERSIH DAN PANAS	DRAWING INFORMATION	PARAF	NO.	DATE REVISION	NO.	DATE REVISION	DATE	CODE	SHEET NUMBER
			DRAWN BY : –		01.	–	04.	–	11/05/23	PL	PL-01
			CHECKED BY : –		02.	–	05.	–			
			P.I.C. : –		03.	–	06.	–	PROJECT NO. : –		