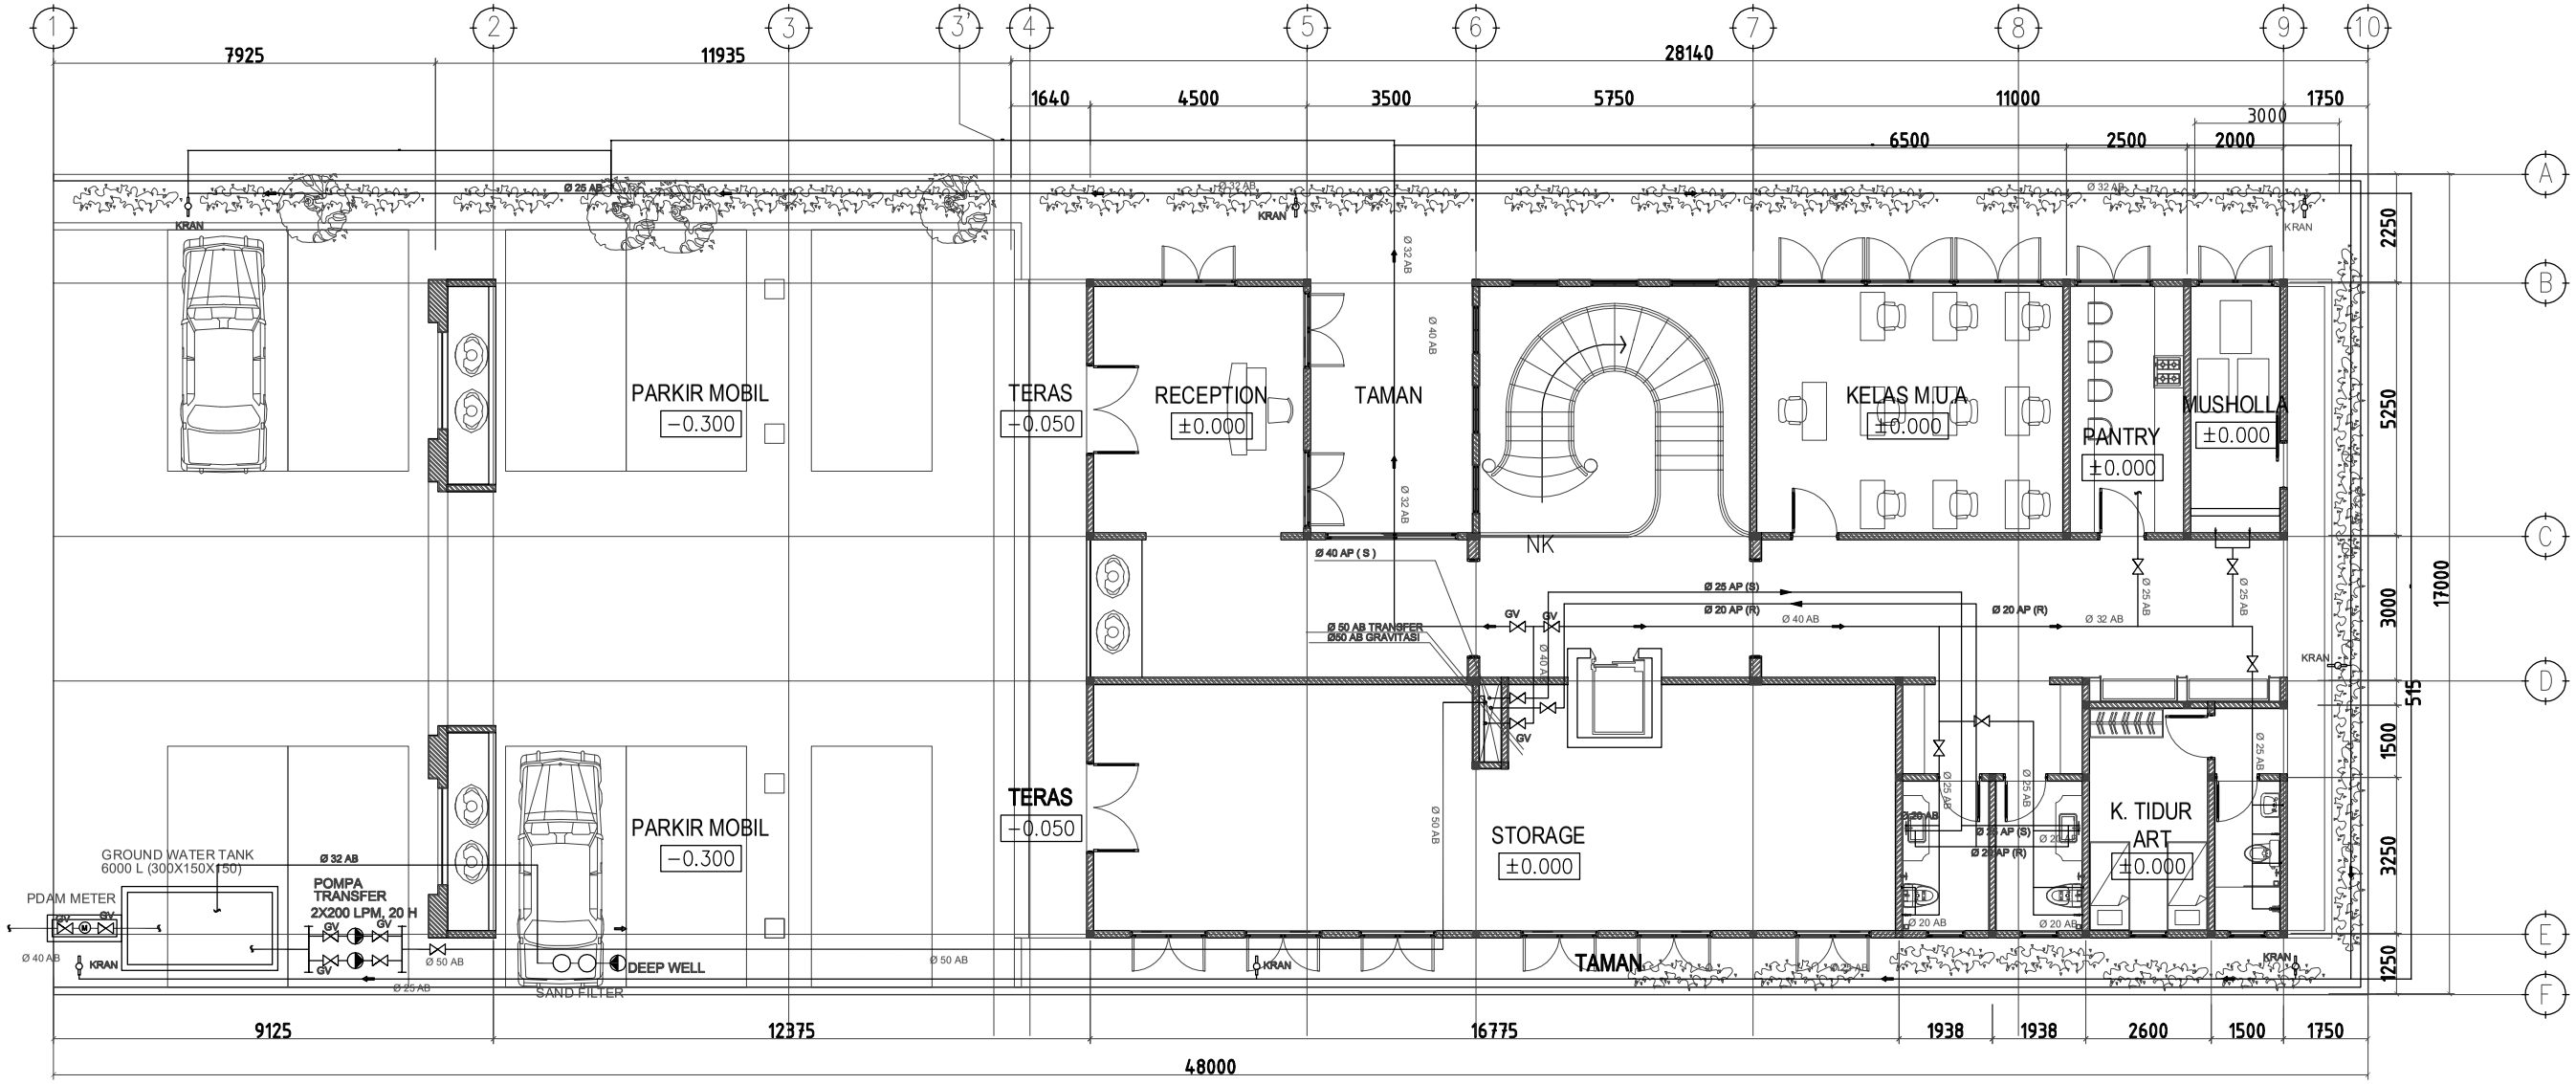

DENAH INSTALASI PIPA AIR BERSIH & PANAS LT.1

SKALA : 1 : 150

FOR CONSTRUCTION

yudha narta
architecture . interior . decoration
email : yudha_gumulja@cbn.net.id

PROJECT :	DRAWING TITLE :	DRAWING INFORMATION	PARAF	NO.	DATE REVISION	NO.	DATE REVISION	DATE	CODE	SHEET NUMBER
DEPOK - JAWA BARAT	DENAH INSTALASI PIPAIR BERSIH DAN PANAS LANTAI 1	DRAWN BY : –		01.	–	04.	–	11/05/23	PL	PL-02
		CHECKED BY : –		02.	–	05.	–			
		P.I.C. : –		03.	–	06.	–	PROJECT NO. : –		